


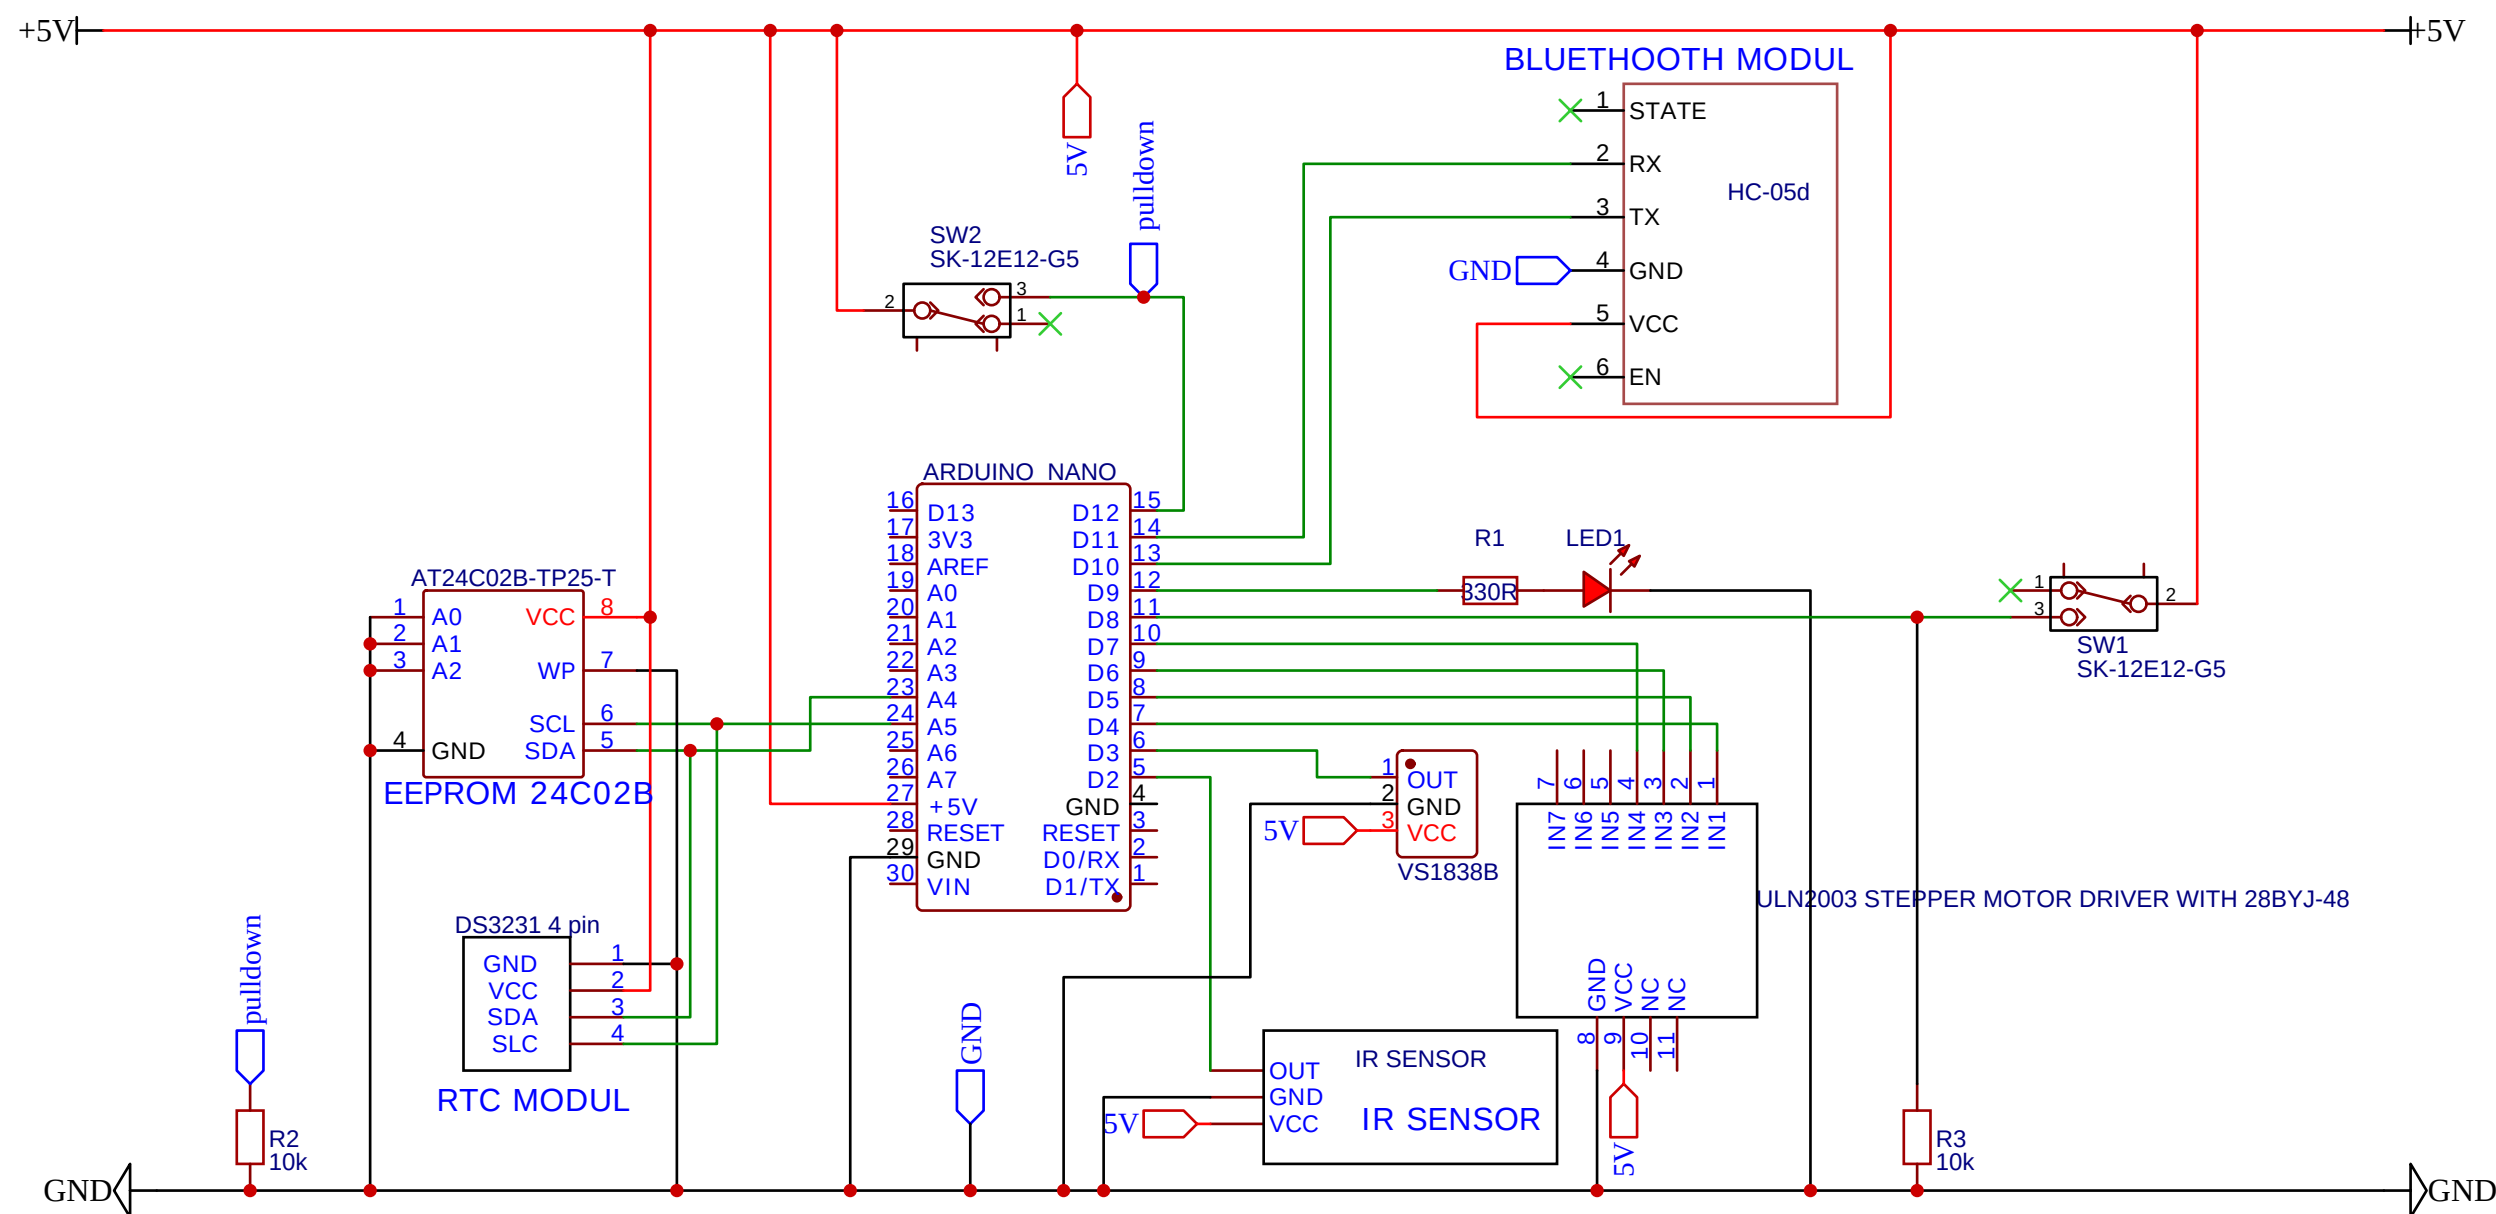

TITLE: navrh zapojeni		REV: 1.0
	Company: S ŠPU Opava	Sheet: 1/1
	Date: 2025-11-11 Drawn By: sarkazurkova	